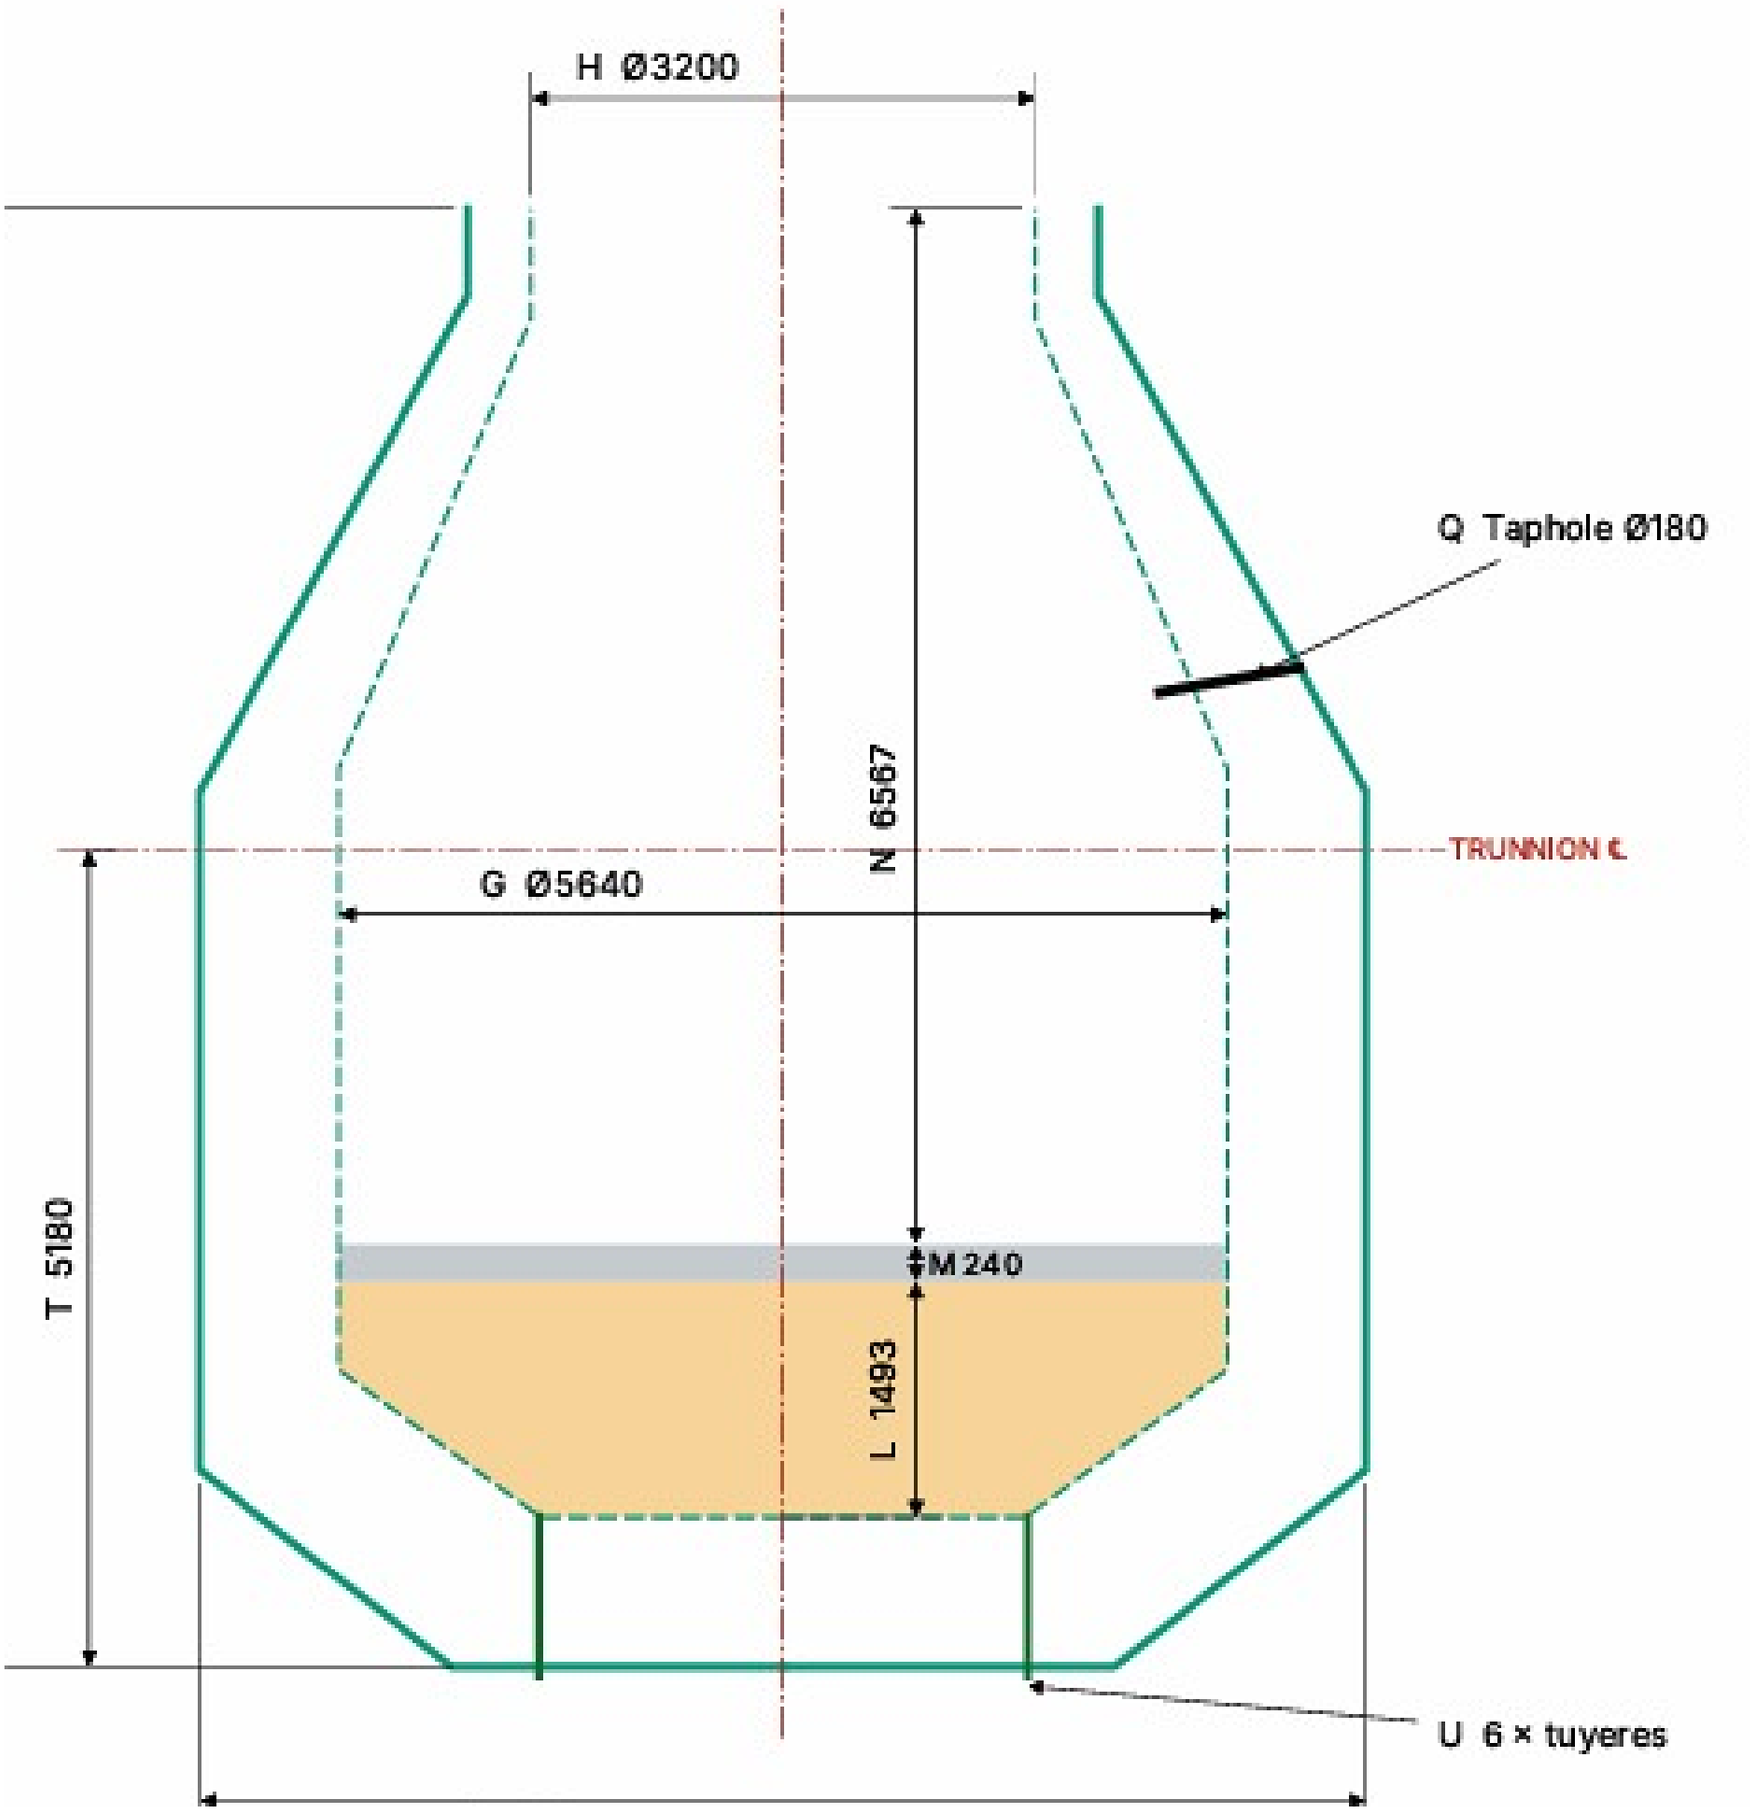

H Ø3200
Q Taphole Ø180
N 6567
TRUNNION €
G Ø5640
T 5180
M 240
L 1493
U 6 × tuyeres